



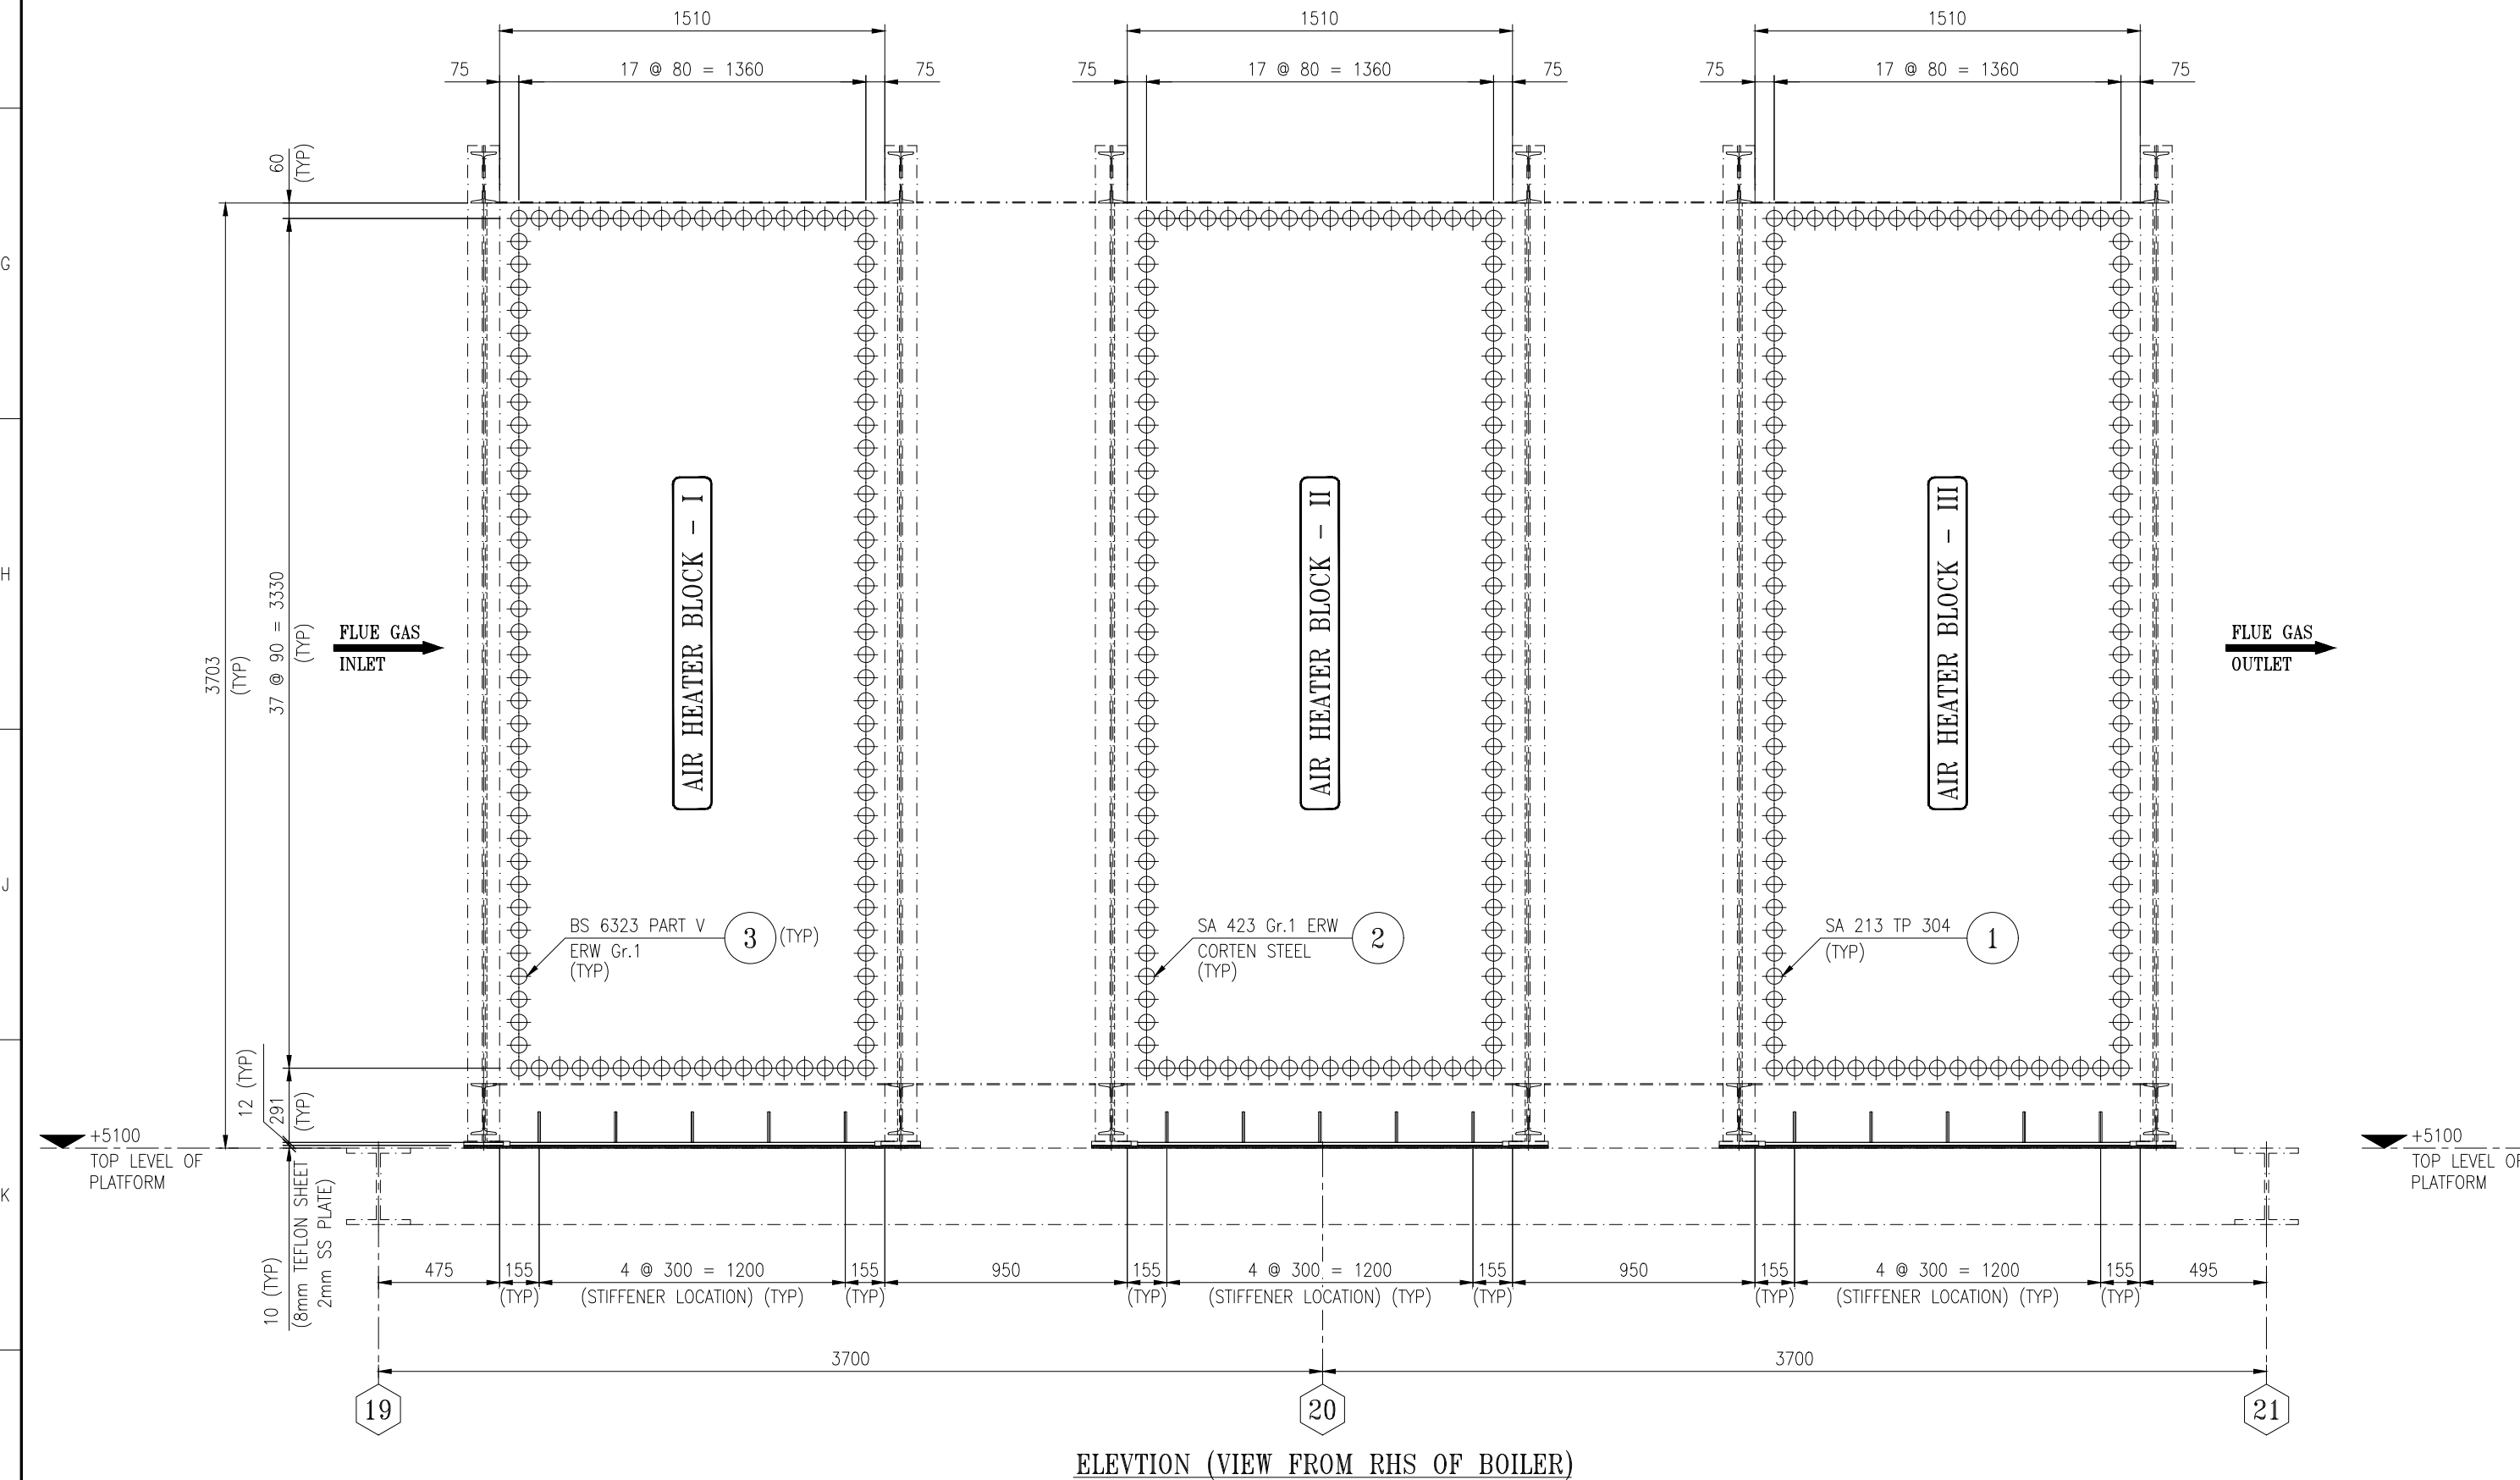


ELEVATION (VIEW FROM RHS OF BOILER)

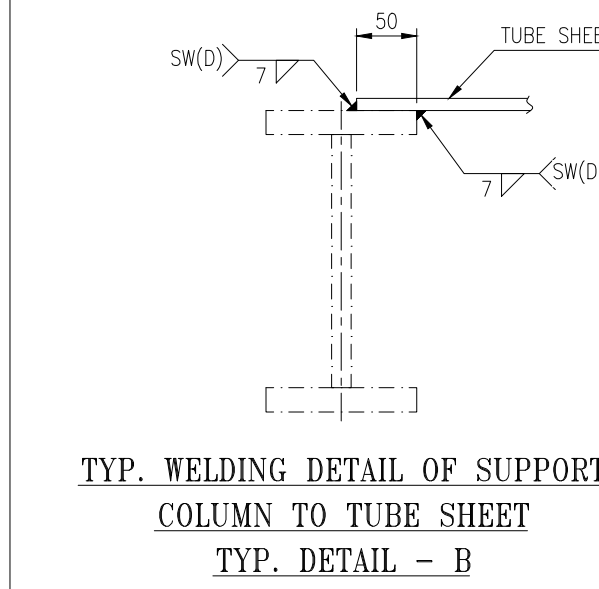

TYP. SECTION THROUGH TUBE SHEET
(SHOWING AIR HEATER
TUBE EXPANSION & WELDING)

TYP. DETAIL - A
(FOR AIR HEATER BLOCK - III INLET ONLY)

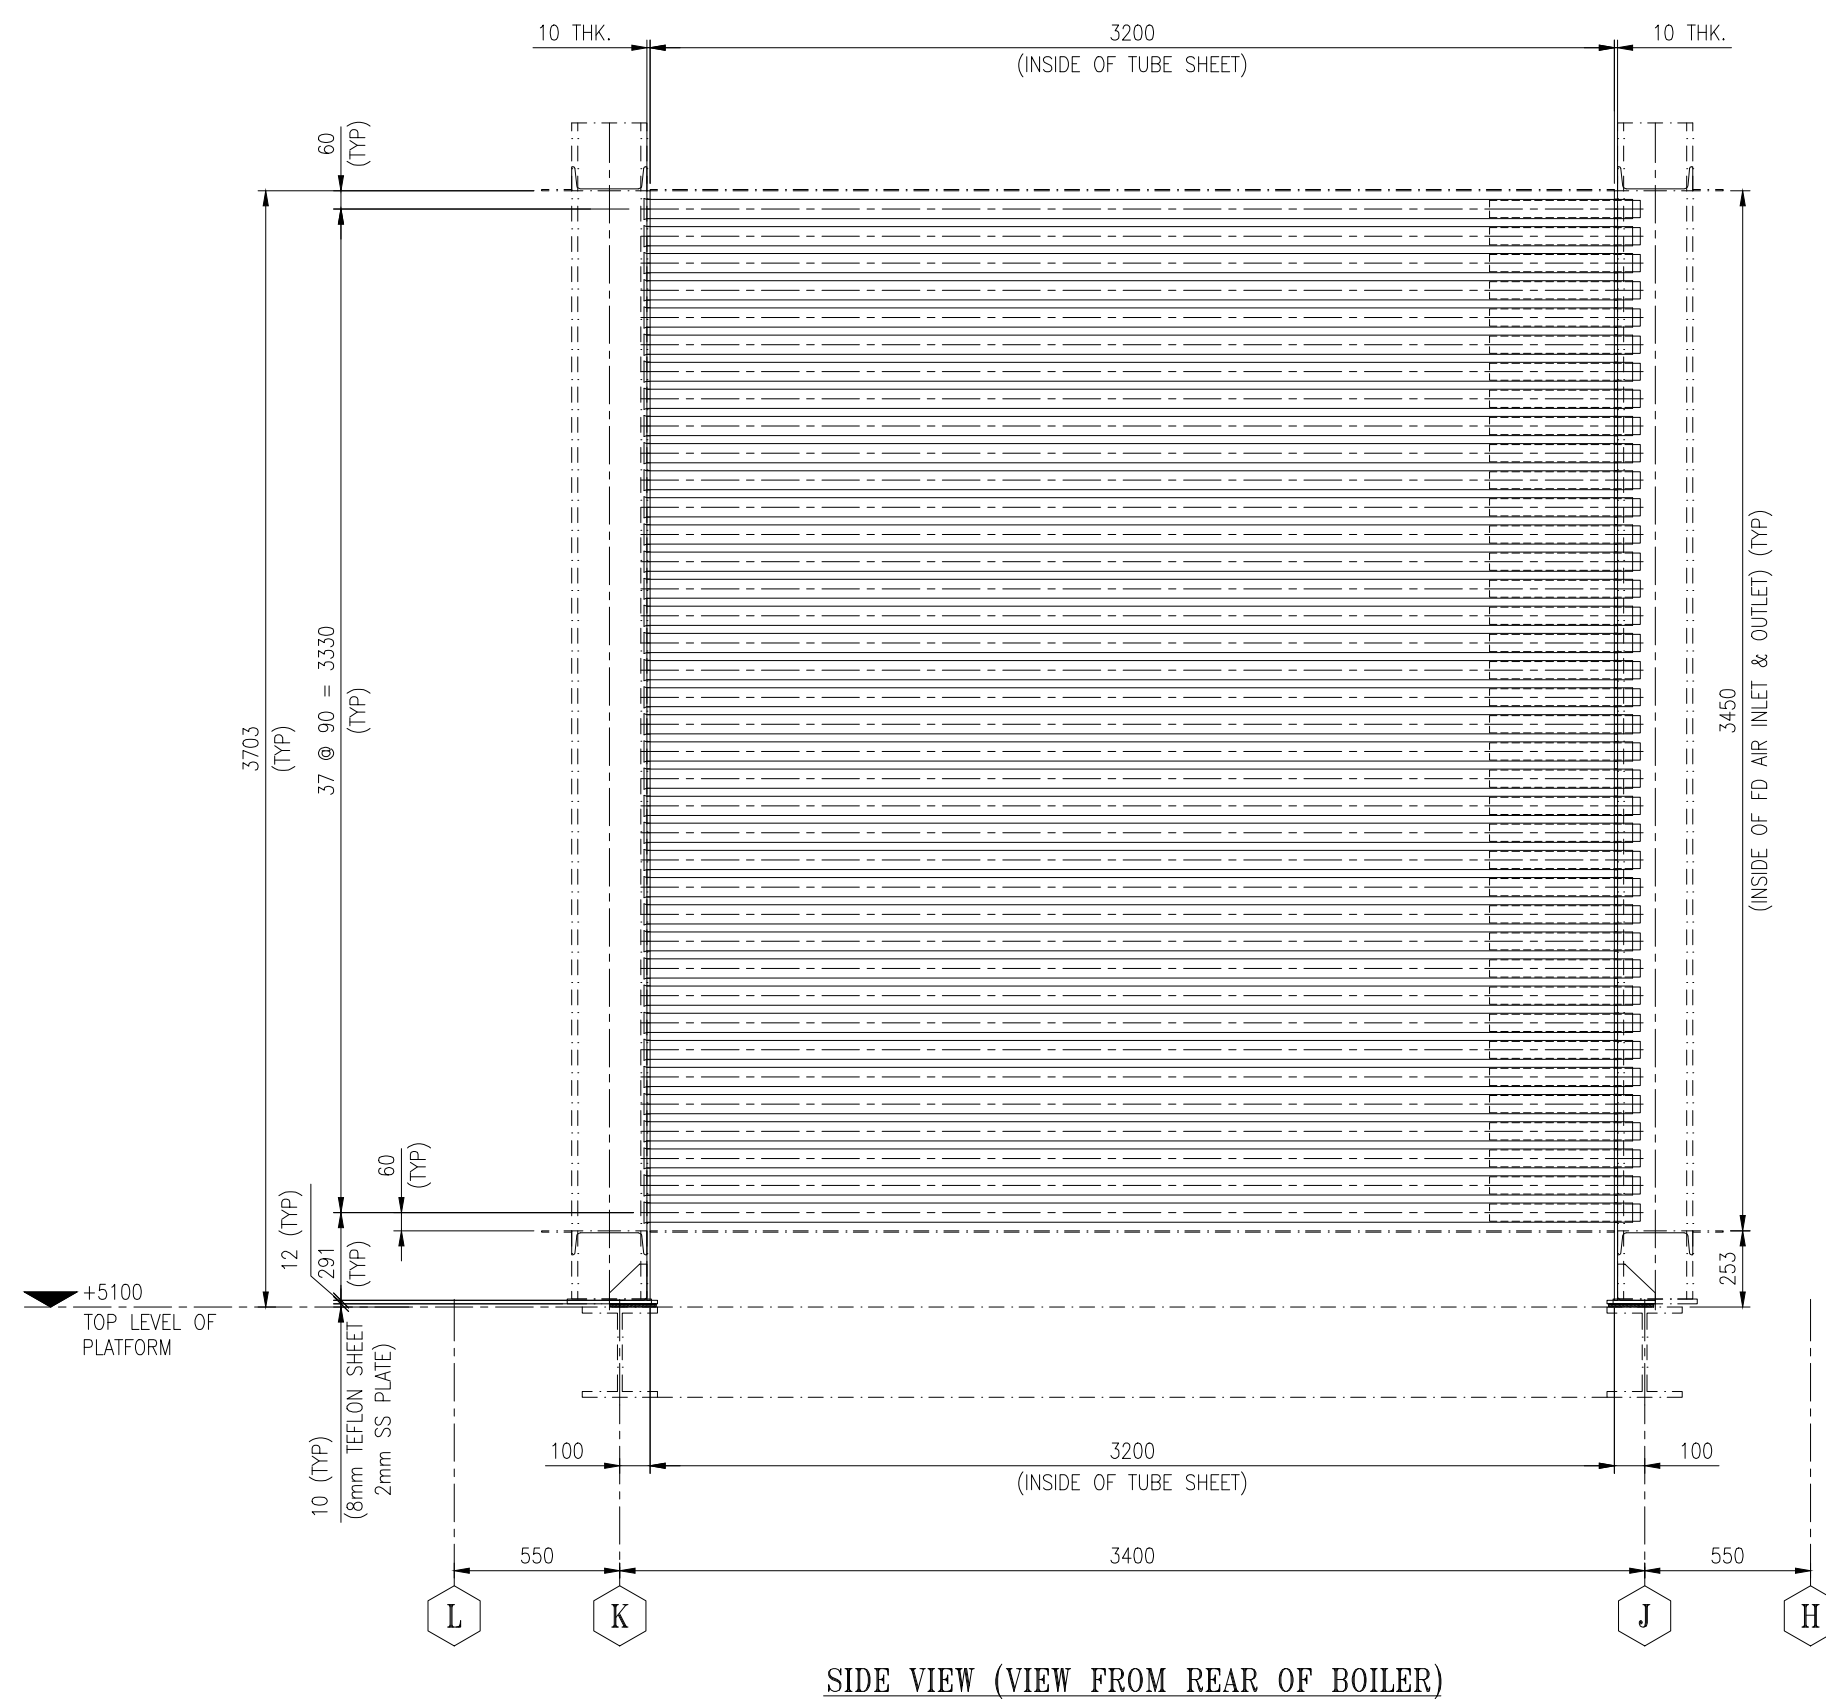

SIDE VIEW (VIEW FROM REAR OF BOILER)

01. ALL DIMENSIONS ARE IN "mm" UNLESS OTHERWISE SPECIFIED.
02. HOLE TOLERANCE OF ± 0.4 TO BE STRICTLY MAINTAINED.
03. FABRICATION TO BE DONE BY FULL SCALE SHOP LAYOUT.
04. DENOTES: FW - FIELD WELD; SW-DENOTES FABRICATION SHOP WELD; SW(D) - SHOP WELD DAHEJ.
05. TUBE HOLE & TUBE ENDS ARE TO BE THOROUGHLY CLEANED BEFORE EXPANSION AT DAHEJ.
06. WELDING ELECTRODE SHALL BE IS-814 (LATEST).
07. ALL WELDING SHALL BE DONE AS PER IS:816 & 823 & SHALL BE FULL CONTACT LENGTH UNLESS STATED OTHERWISE.
08. ALL STRUCTURAL MEMBERS CONFORM TO IS:808.
09. SURFACE FINISH OF TUBES (50mm at BOTH ENDS) TO BE MAINTAINED AS 120 MICRONS INCHES.
10. ALL TUBE PLATES & TUBES TO HAVE THEIR RESPECTIVE I.W.T No. & P.No. PAINTED ON IN WHITE WATER PROOF PAINT.
11. IN AIR HEATER TUBE SHEETS HOLE APPLY RUST PREVENTIVE OIL BEFORE DESPATCH.
12. AIR HEATER TUBES (ITEM CODE : AH001, AH002 & AH003) ARE RELEASED AS BOUGHT OUT ITEMS ALONG WITH OUR AIR HEATER TUBE SPECIFICATION JB1002-50050100-SPC-0000.
13. FOR DIMENSIONAL TOLERANCE REQUIREMENT PLEASE REFER DOC.No. GEN-50020100-DSM-002 AND ITS ASSOCIATED DRAWING.

01. ALL WELDING SHOULD BE SOUND AND COMPLETE WITHOUT ANY GAP, TO AVOID LEAKAGE OF AIR FROM ONE SIDE TO ANOTHER.
02. SLEEVES TO BE PROVIDED AT AIR HEATER BLOCK-III, AIR ENTRY INSIDE ONLY.
03. AFTER THE INSERTION OF AIR HEATER TUBE, THE SLEEVE WITH ATTACHMENT CLIP TO BE WELDED AT DAHEJ.
04. CASING INSIDE SEAL WELD TO BE DONE AT DAHEJ BEFORE ERECTION OF AIR HEATER TUBE.
05. AIR HEATER TUBES SHALL BE PROTECTS USING END CAPS SUPPLIED ALONG WITH THEM BEFORE APPLICATION OF REFRACTORY.


01. REFER DOCUMENT No: JB1002-50570902-PSH-0001 FOR PAINTING SCHEDULE.

AHT003	03	AIR HEATER TUBE - I	JS 623 PART V EW 01	QD 63.5 x 2.03 THK x 3240 LG	692	6899.24	ACTUAL+ERLECTION SPREAD (8 No)	
		AIR HEATER TUBE BLOCK - I	P	B006	692	6899.24		
AHT002	02	AIR HEATER TUBE - II	SA 423 Gr.1 ERW	QD 63.5 x 2.03 THK x 3240 LG	692	6899.24	ACTUAL+ERLECTION SPREAD (8 No)	
		AIR HEATER TUBE BLOCK - II	P	B006	692	6899.24		
AHT001	01	AIR HEATER TUBE - III	SA 213 TP 304	QD 63.5 x 2.03 THK x 3280 LG	692	7148.36	ACTUAL+ERLECTION SPREAD (8 No)	
		AIR HEATER TUBE BLOCK - III	P	B006	692	7148.36		
P.NO.		P.DESCRPTION		SIZE		P.Q'TY	P.WT(kg)	REMARK
ITEM CODE	ITEM DESCRIPTION			1.TYPE	1.GROUP	1.QTY	1.WT(kg)	REMARK

FOR AIR HEATER TUBES REFER SPEC. DOCUMENT ID - JB1002-50050100-SPC-0001

REV.	ZONE	DESCRIPTION	REVD. BY	CHKD. BY	APPD. BY	DATE

CONSULTANT		—										
CLIENT		TSK ELECTRONICA Y ELECTRICIDAD, S.A.										
DO NOT SCALE IF IN DOUBT PLEASE ASK		THIS DESIGN IS THE PROPERTY OF M/S. ISGEC HEAVY ENGINEERING LTD. AND IS ONLY ALLOWED TO BE USED BY EXPRESSED PERMISSION AND LICENSE FROM M/S. ISGEC HEAVY ENGINEERING LTD.										
		FOR APPROVAL		NO	FOR INFORMATION		NO	FOR PRODUCTION		YES	FOR ERECTION	
RESPONSIBLE DEPT. MECHANICAL		DRAWN BY P.SHANMUGAVEL		CHECKED BY BSV/RAMUDU			APPROVED BY R.ARUN/S.SEN			DATE 25.09.2017		
 	TOTAL WEIGHT IN kg. 20946.84			PROJECT ID JB1002			ELEMENT ID 50050100			I.W.T. NO. 6503		
				YEAR : 2016			SHEET SIZE : A1			SCALE : 1:25		

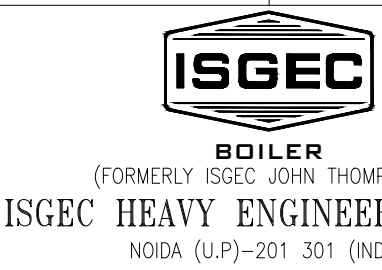

 ISGEC (FORMERLY ISGEC JOHN THOMPSON) ISGEC HEAVY ENGINEERING LTD. NOIDA (U.P.)-201 301 (INDIA)	SERVICE	Durrah Sugar Refinery (Yanbu-KSA)		
	TITLE	ARRANGEMENT AND DETAIL OF AIR HEATER		
	DRAWING DOCUMENT ID	JB1002-50050100-038-0001	REVISION	00



	FORMAT A-1	SCALE 1:25
---	---------------	---------------

CLIENT:	 شركة الدرة المتقدمة Durrah Advanced Development Co.	CONSULTANT:	 JFMA	CLIENT Nr.	-
PROJECT:	Durrah Sugar Refinery (Yanbu - KSA)			TSK Nr.	-
				REVISION	00
DRAWING TITLE:	ARRANGEMENT AND DETAIL OF AIR HEATER			SUBCONTRACTOR Nr.	JB1002-50050100-038-0001
				REVISION	00
SHEET 1 TO 1				PROJECT Nr.	000659

THE INFORMATION CONTAINED IN THIS DOCUMENT IS CONFIDENTIAL AND RESTRICTED, AND IS TO BE USED ONLY FOR THE PURPOSES ESTABLISHED IN THE DOCUMENT. NO MODIFICATION, EXPLOITATION, REPRODUCTION, COMMUNICATION TO ANY THIRD PARTY, DISSEMINATION OR DISTRIBUTION OF THE WHOLE OR ANY PART OF THE DOCUMENT IS PERMITTED WITHOUT THE PRIOR, WRITTEN CONSENT OF TSK FAILURE TO RESPOND TO ANY REQUEST FOR SUCH CONSENT SHALL IN NO WAY BE CONSTRUED AS AUTHORIZATION FOR USE.

REV.	DESCRIPTION	DRAWN	CHECKED	APPROVED	DATE
REVISION INDEX					