
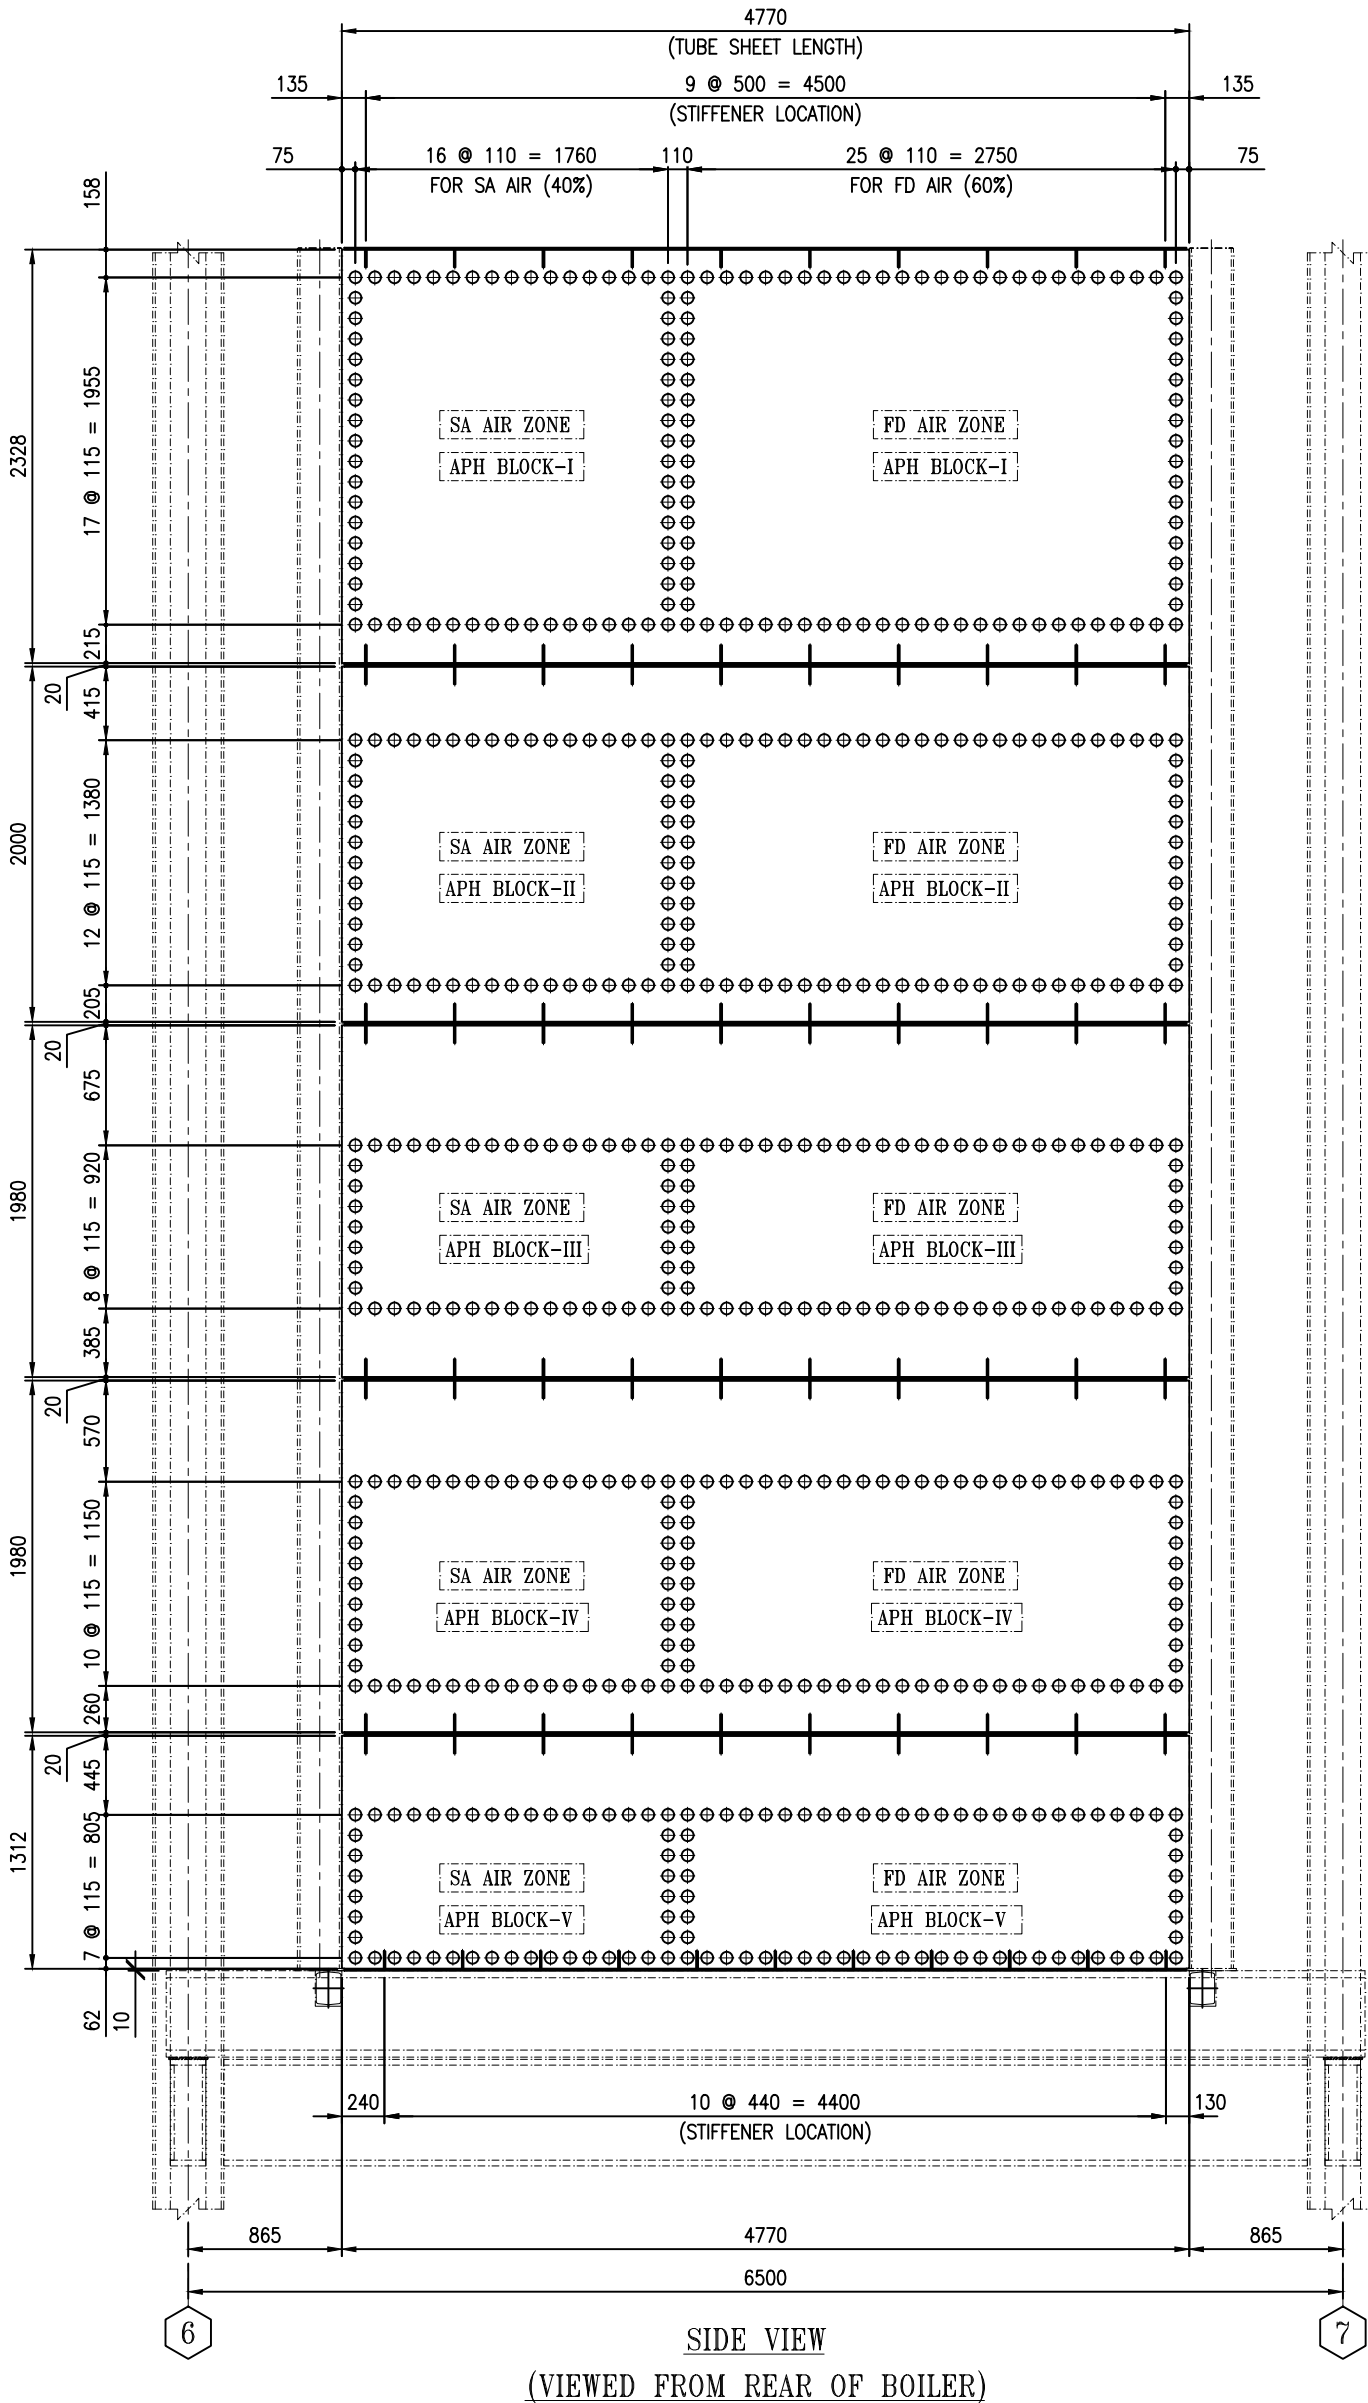
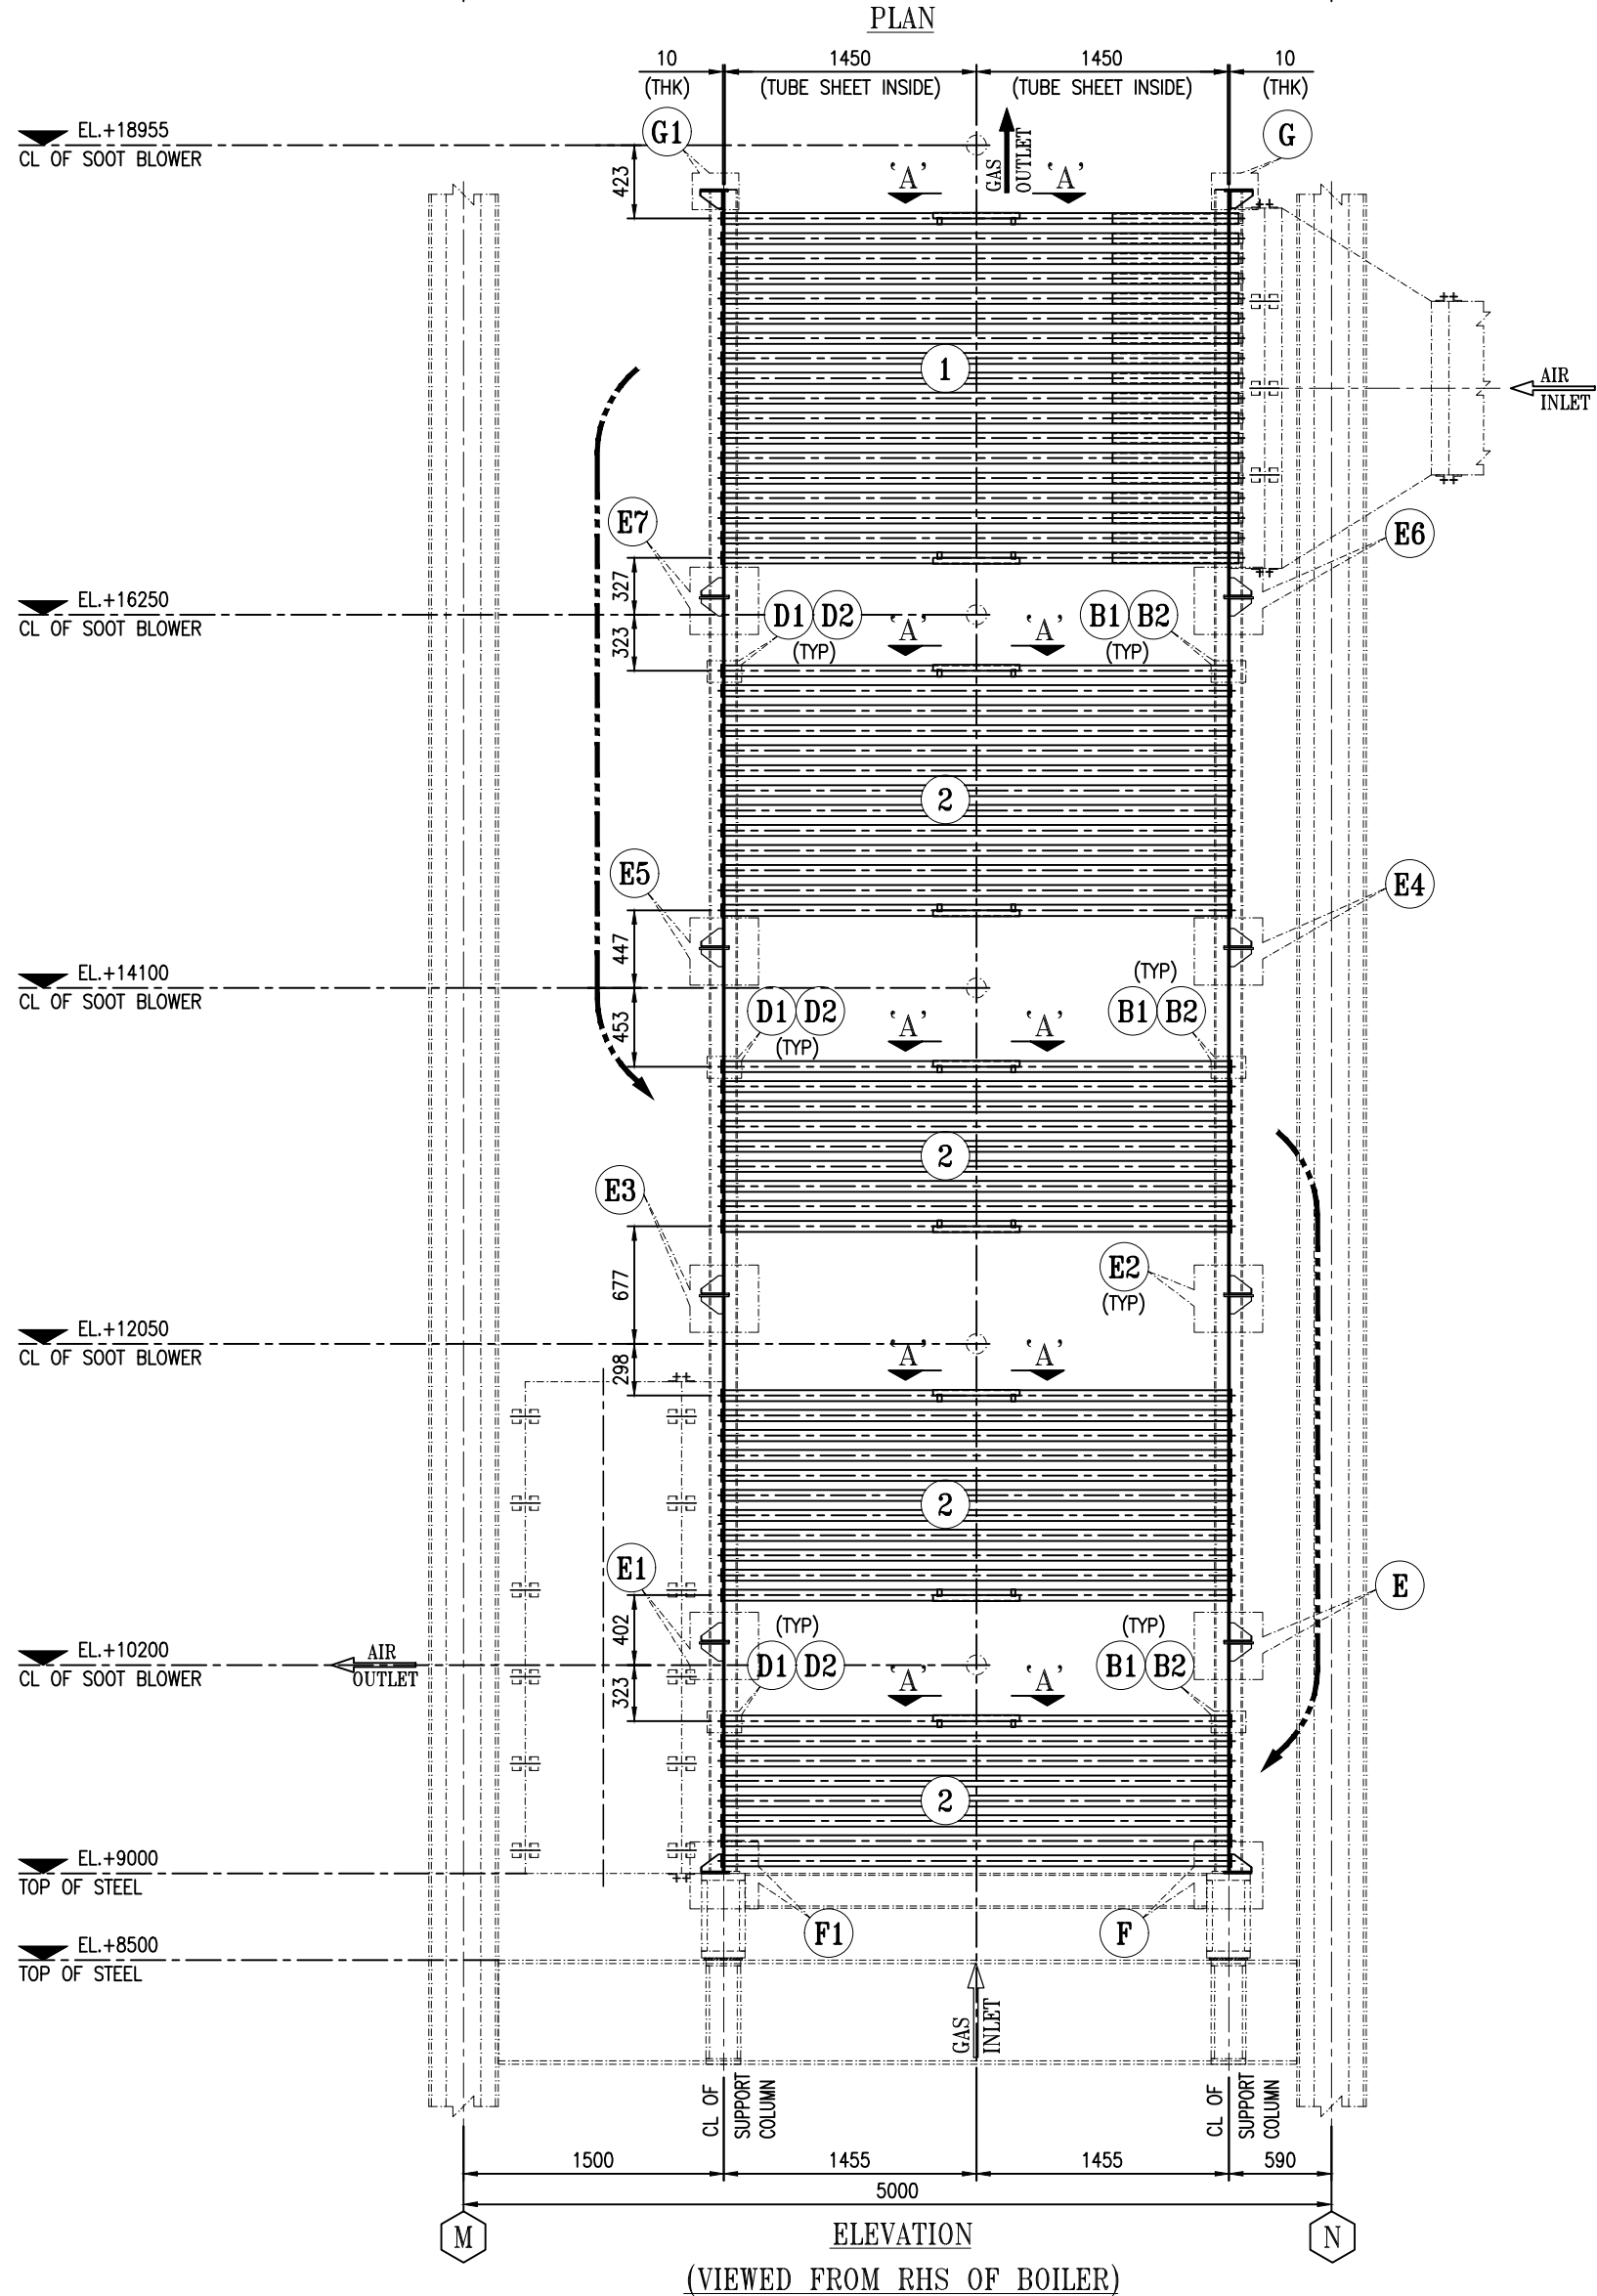


THIS IS A CAD FILE - DO NOT CORRECT IT MANUALLY

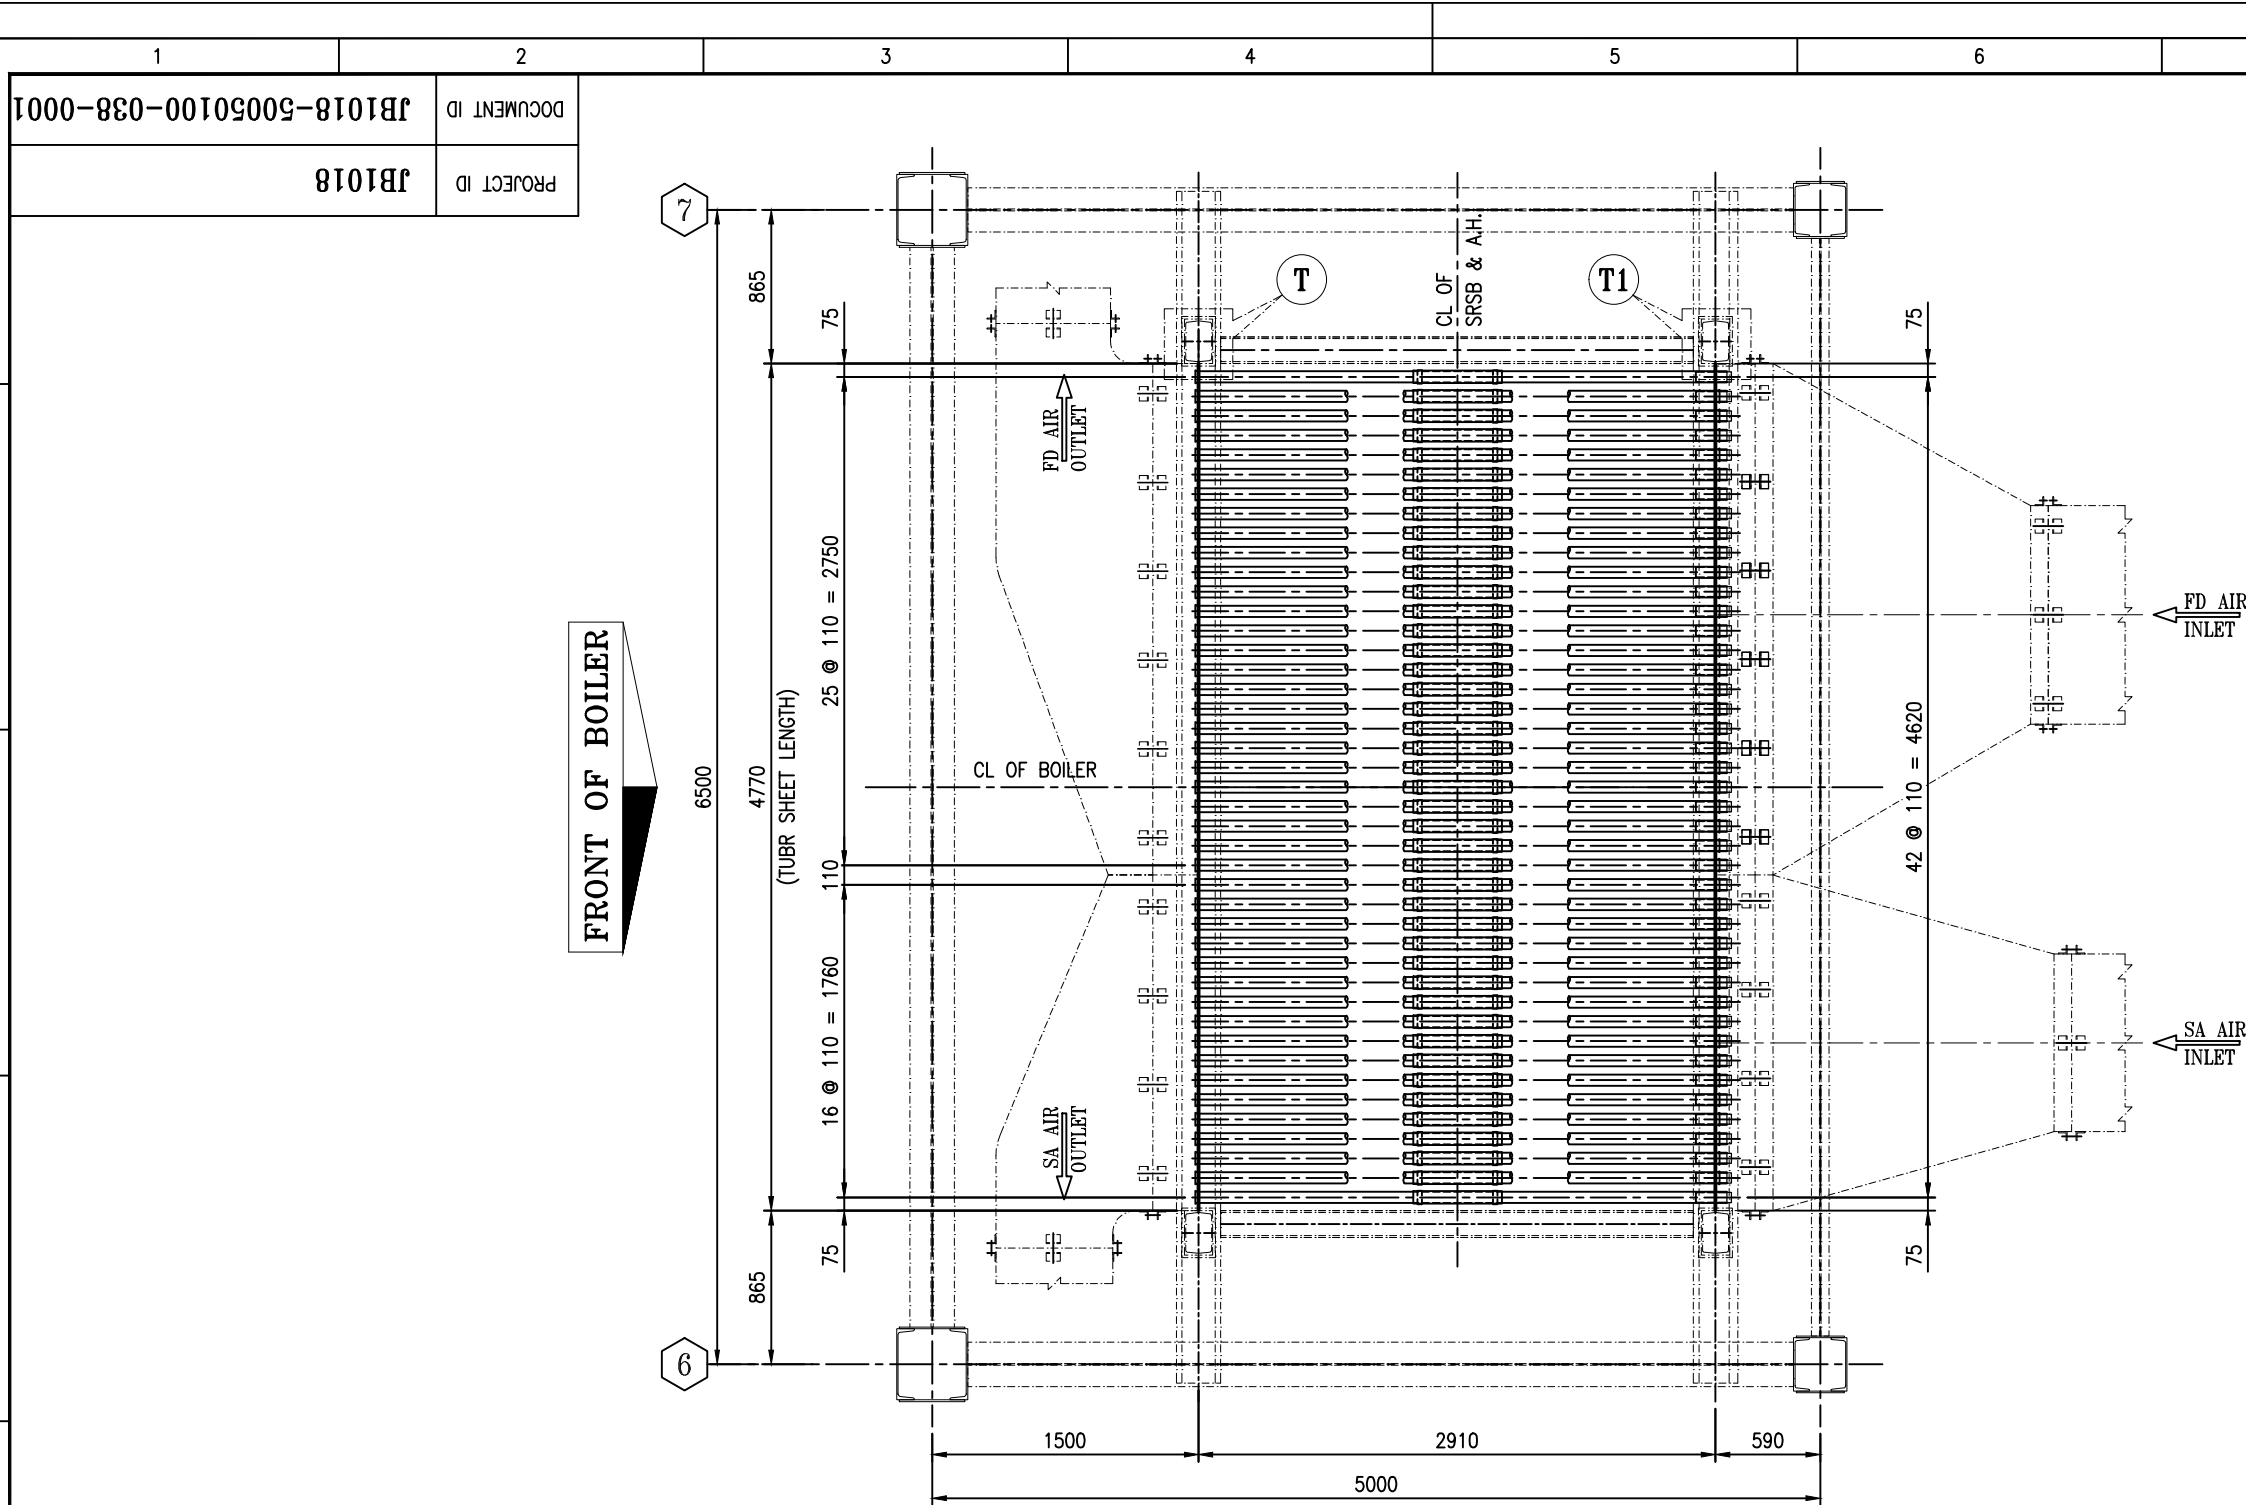

NOTES:-

01. ALL DIMENSIONS ARE IN mm UNLESS OTHERWISE SPECIFIED.
02. HOLE TOLERANCE OF $\phi 63.5^{+0.1}_{-0.1}$ TO BE STRICTLY MAINTAINED.
03. FABRICATION TO BE DONE BY FULL SCALE SHOP LAYOUT.
04. TUBE HOLE & TUBE ENDS ARE TO BE THOROUGHLY CLEANED BEFORE EXPANSION AT SITE.
05. I/S - DENOTES INSIDE DIMENSIONS, FW - DENOTES FIELD WELD.
06. WELDING ELECTRODE SHALL CONFORM TO IS-814 (LATEST).
07. ALL WELDING SHALL BE DONE AS PER IS-816 & 823 & SHALL BE FULL CONTACT LENGTH UNLESS STATED OTHERWISE.
08. ALL STRUCTURAL MEMBERS CONFORM TO IS-808.
09. SURFACE FINISH OF TUBES (50mm AT BOTH ENDS) TO BE MAINTAINED AS 120 MICRONS INCHES.
10. FOR DIMENSIONAL TOLERANCE REQUIREMENT PLEASE REFER DOC.No. GEN-50990100-DSM-002 AND ITS ASSOCIATED DRAWING.
11. AIR HEATER TUBES (ITEM CODE : AH001 & AH002) SLEEVE (ITEM CODE : AH003) ARE RELEASED AS BOUGHT OUT ITEMS ALONG WITH OUR AIR HEATER TUBE SPECIFICATION JB1018-50050100-SPC-0001.
12. BOTH TUBE SHEET OF EACH AIR HEATER BLOCK TO BE CLAMPED TOGETHER AND STACK DRILLED TO ENSURE THAT ALL TUBE HOLES COINCIDE.
13. IN AIR HEATER TUBE SHEET HOLES APPLY RUST PREVENTIVE OIL BEFORE DESPATCH.

PAINTING NOTES:-

FOR PAINTING NOTES REFER SPECIFICATION No: JB1018-50570900-PSH-0001.

ERECTION NOTES:-

01. ALL WELDING SHOULD BE SOUND AND COMPLETE WITHOUT ANY GAP, TO AVOID LEAKAGE OF AIR FROM ONE SIDE TO ANOTHER.
02. REFRACTORY TO BE APPLIED BEFORE ERECTING COLD AIR DUCT.
03. CASING INSIDE SEAL WELD TO BE DONE AT SITE BEFORE ERECTION OF AIR HEATER TUBE.
04. SLEEVES TO BE PROVIDED AT AIR HEATER BLOCK-I, AIR ENTRY INSIDE ONLY.
05. SLEEVES ARE TO BE INSERTED & WELDED WITH TUBES AFTER REFRACTORY APPLICATION.
06. ON COMPLETION OF REFRACTORY APPLICATION THE COTTON WASTE SHALL BE REMOVED.
07. INSPECTION BY THE QA ENGINEER FOR 100% REMOVAL OF COTTON WASTE IS REQUIRED.
08. AFTER THE INSERTION OF AIR HEATER TUBE, THE SLEEVE WITH ATTACHMENT CLIP TO BE WELDED AT SITE.
09. AIR HEATER TUBES SHALL BE PROTECTED USING END CAPS SUPPLIED ALONG WITH THEM BEFORE APPLICATION OF REFRACTORY.

LIST OF REFERENCE DRAWINGS

DRAWING DOCUMENT ID	DESCRIPTION
JB1018-50050100-038-0002	DETAIL OF AIR HEATER
JB1018-50050100-038-0003	DETAIL OF AIR HEATER TUBE SHEET
BIS-RPC-001-32-S1	EROSION PROTECTION ATTACHMENT CLIP FOR TUBE $\phi 63.5$ (FOR AIR HEATER TUBES)
BIS-RPS-001-31-S1	EROSION PROTECTION SLEEVE FOR TUBE $\phi 63.5$ (FOR AIR HEATER TUBES)

FOR AIR HEATER TUBES REFER SPEC. DOCUMENT ID - JB1018-50050100-SPC-0001

THIS DRAWING SHOULD BE READ IN CONJUNCTION WITH DWG. No.
JB1018-50110107-040-0001 (AIR HEATER CASING)

RPSAH202511A	ATTACHMENT CLIP ($\phi 63.5 \times 25$ Lg.) P.No. 10	S	B006	790	55.30	16 Nos. EXTRA REF. DRG. (BIS-RPC-001-32-S1)
RPSAH250011A	HALF SLEEVE ($\phi 63.5 \times 500$ Lg.) P.No. 9	S	B006	395	513.50	8 Nos. EXTRA REF. DRG. (BIS-RPS-001-31-S1)

ITEM CODE	ITEM DESCRIPTION	I.TYPE	I.GROUP	I.QTY	I.WT (Kg)	REMARK
-----------	------------------	--------	---------	-------	-----------	--------

MATERIAL LIST (FOR STANDARD ITEMS)

3	SLEEVE TUBE	IS 633 PHF-4, 182 Q211	O/D 57.15 X 2.03 THK x 3015 Lg.	195	1622.40	ACTUAL ERECTION SPARE (15 Nos.) (SLEEVES FOR AH001 TUBES)
AH003	AIR HEATER TUBE SLEEVE	P	B006	195	1622.40	
2	AIRHEATER TUBE BLOCK-I/II/III & V	IS 633 PHF-4, 182 Q211	O/D 63.5 X 2.34 THK x 2940 Lg.	1800	18677.70	ACTUAL ERECTION SPARE (37 Nos.)
AH002	AIR HEATER TUBE	P	B006	1800	18677.70	
1	AIRHEATER TUBE BLOCK-I	SA 423 Gr.1ERW	O/D 63.5 X 2.34 THK x 2980 Lg.	790	8309.00	ACTUAL ERECTION SPARE (16 Nos.)
AH001	AIR HEATER TUBE	P	B006	790	8309.00	
P.No.	P.DESCRPTION	SPECIFICATION	SIZE	P.QTY	P.WT(kg)	REMARK
ITEM CODE	ITEM DESCRIPTION	I.TYPE	I.GROUP	I.QTY	I.WT(kg) (TOTAL)	REMARK

CONSULTANT		M/s. AVANT-GARDE ENGINEERS AND CONSULTANTS (P) LTD.								
CLIENT		M/s. DSCL SUGAR - HARIAWAN								
DO NOT SCALE IF IN DOUBT PLEASE ASK		THIS DESIGN IS THE PROPERTY OF M/S. ISGEC HEAVY ENGINEERING LTD. AND IS ONLY ALLOWED TO BE USED BY EXPRESSED PERMISSION AND LICENSE FROM M/S. ISGEC HEAVY ENGINEERING LTD.								
FOR APPROVAL		NO	FOR INFORMATION		NO	FOR PRODUCTION		YES	FOR ERECTION	
RESPONSIBLE DEPT.		DRAWN BY		CHECKED BY		APPROVED BY		DATE		
MECHANICAL		SV.KUMAR		RAMJUDH/RARUN		S.S.SEN		03.03.2017		
		TOTAL WEIGHT IN kg.		PROJECT ID		ELEMENT ID		I.W.T. NO.		
		29177.90		JB1018		50050100		6516		
		YEAR : 2017		SHEET SIZE : A1		SCALE : 1:40				



ISGEC
(formerly Isgac John Thompson)

Isgec Heavy Engineering Ltd.
Noida 201 301 (U.P.) India

SERVICE
1 x 55 TPH, SINGLE DRUM, GIRTH SUPPORTED, SLOP FIRED TRAVELLING GRATE BOILER

TITLE
GENERAL ARRANGEMENT OF AIR HEATER

DRAWING DOCUMENT ID
JB1018-50050100-038-0001

REVISION
00

REV.	ZONE	DESCRIPTION	REV.	ZONE	DESCRIPTION
------	------	-------------	------	------	-------------